
Emma Steyn
11 September 2026

ste0st24

Kommetjie
Competition
Elective

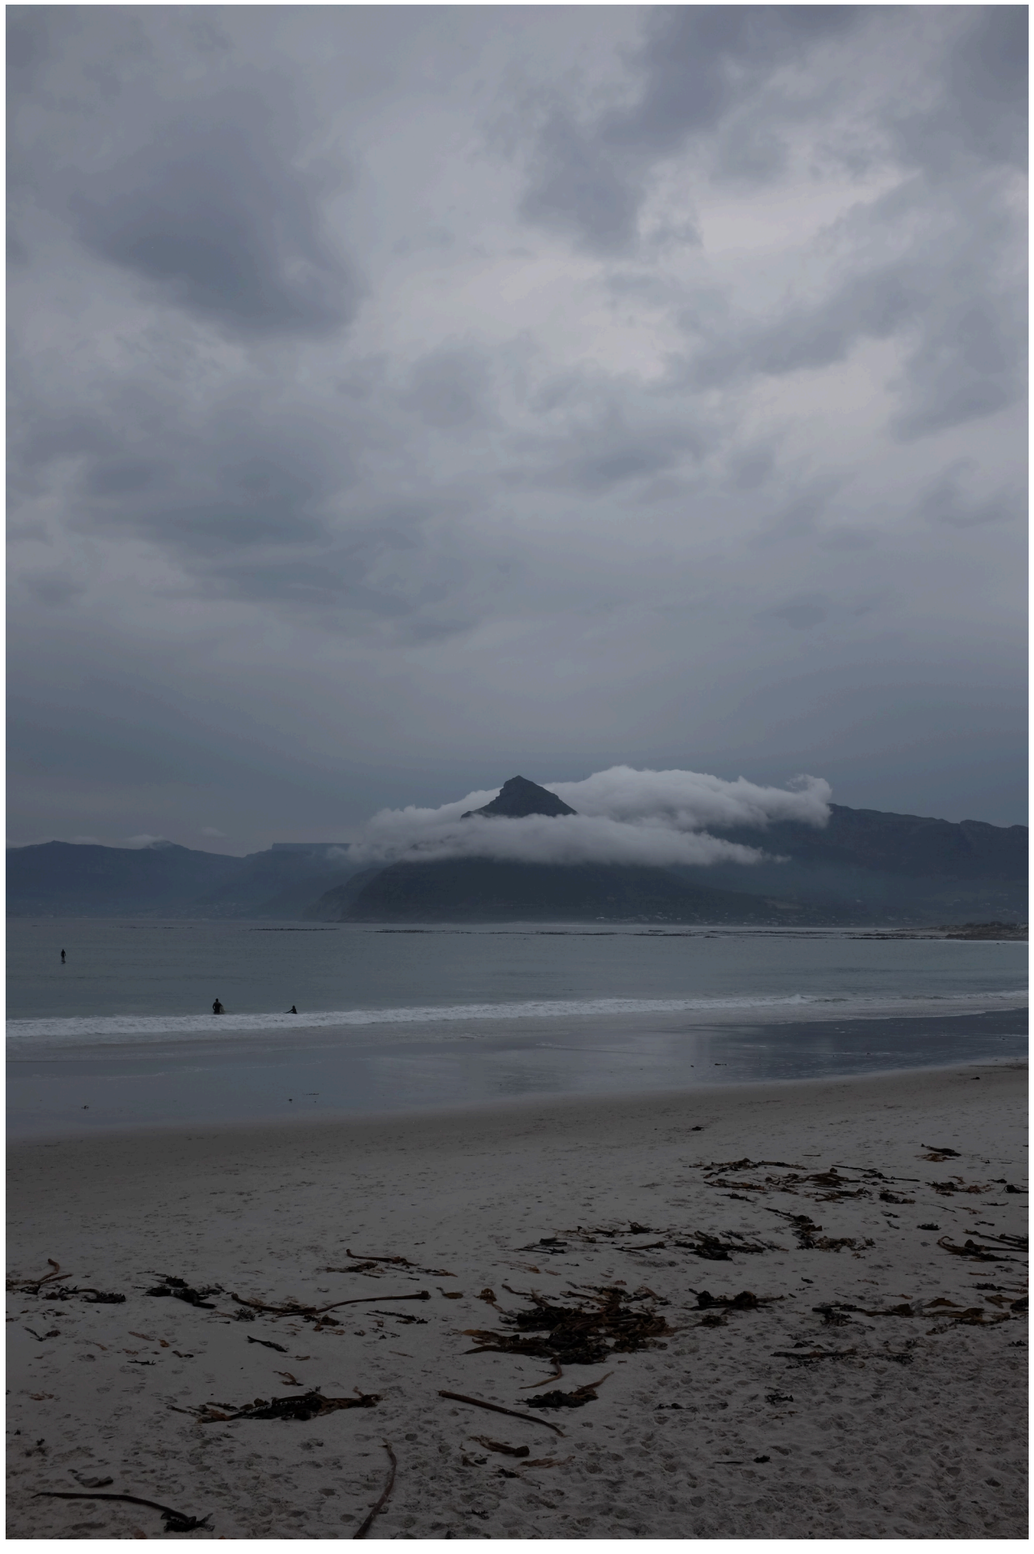

KELP LINE

Long Beach, Kommetjie



1 Surf Way

A new multipurpose civic hub on Kommetjie’s shoreline.

34°08′14″ S · 18°19′42″ E

Place


Site Plan 1:500





1 Surf Way,
Kommetjie,
Western Cape,
South Africa


Site Analysis


Site Plan 1:500

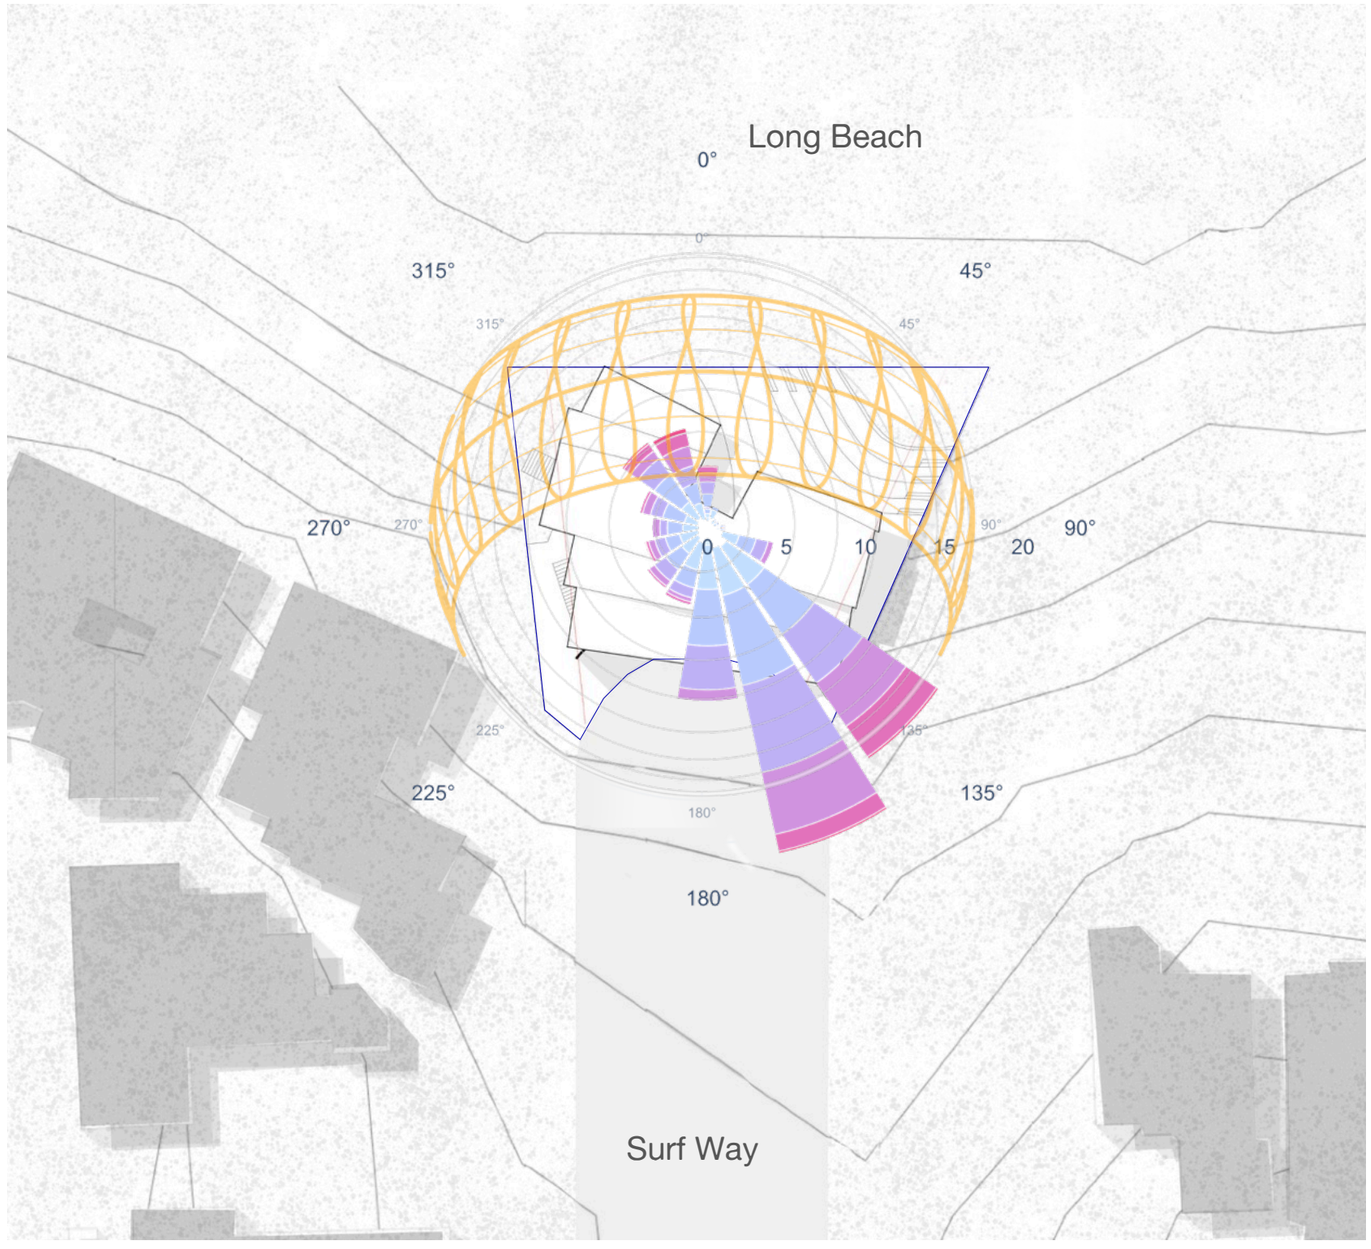

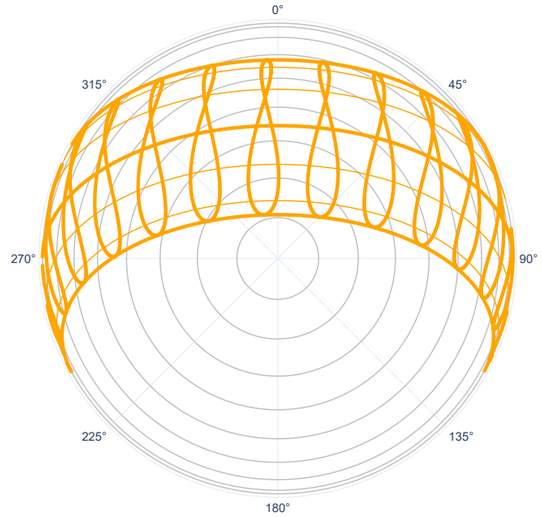


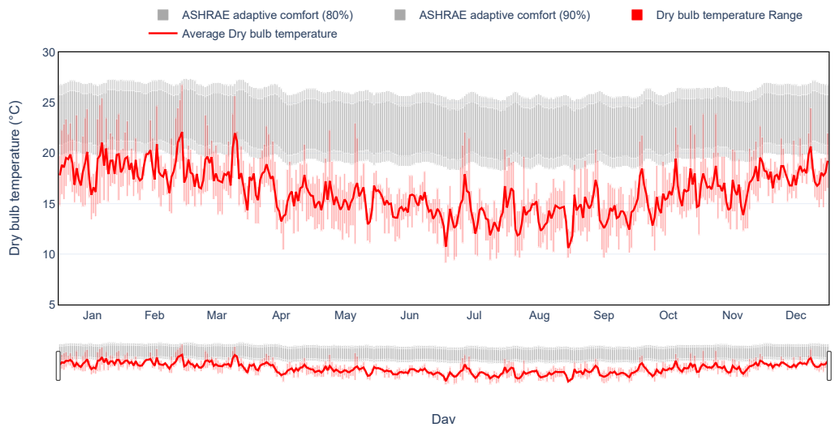

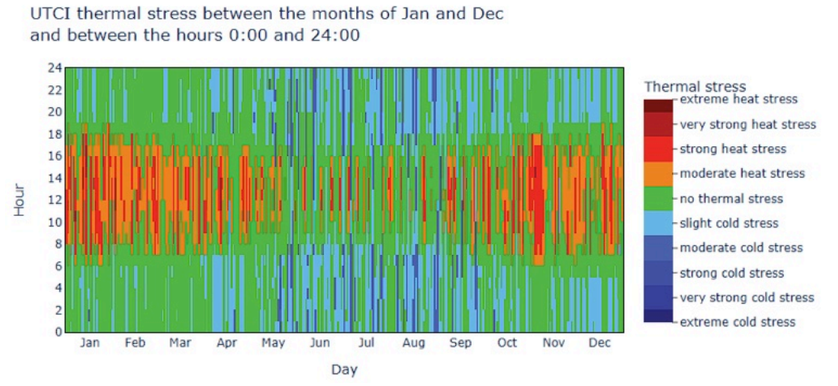

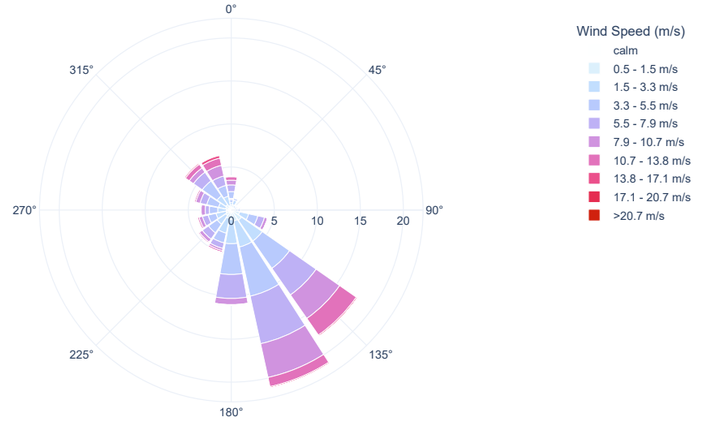

Site Photos

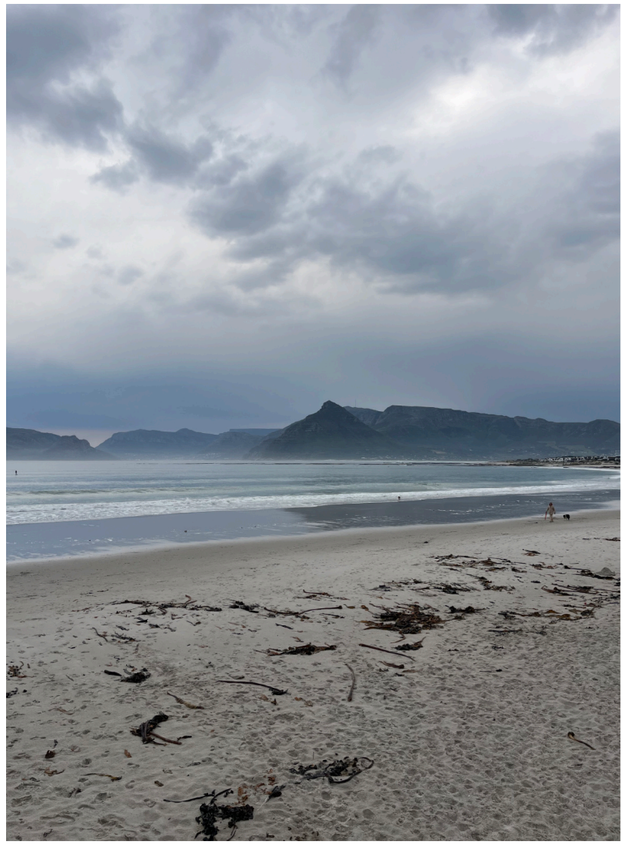




















©jacques de vos





Material Pallette



Eucalyptus Panels



Steel



Natural Stone

Ground Floor Plan


1:200



Ground Floor Plan

Spatial Analysis 1:200

Long Beach

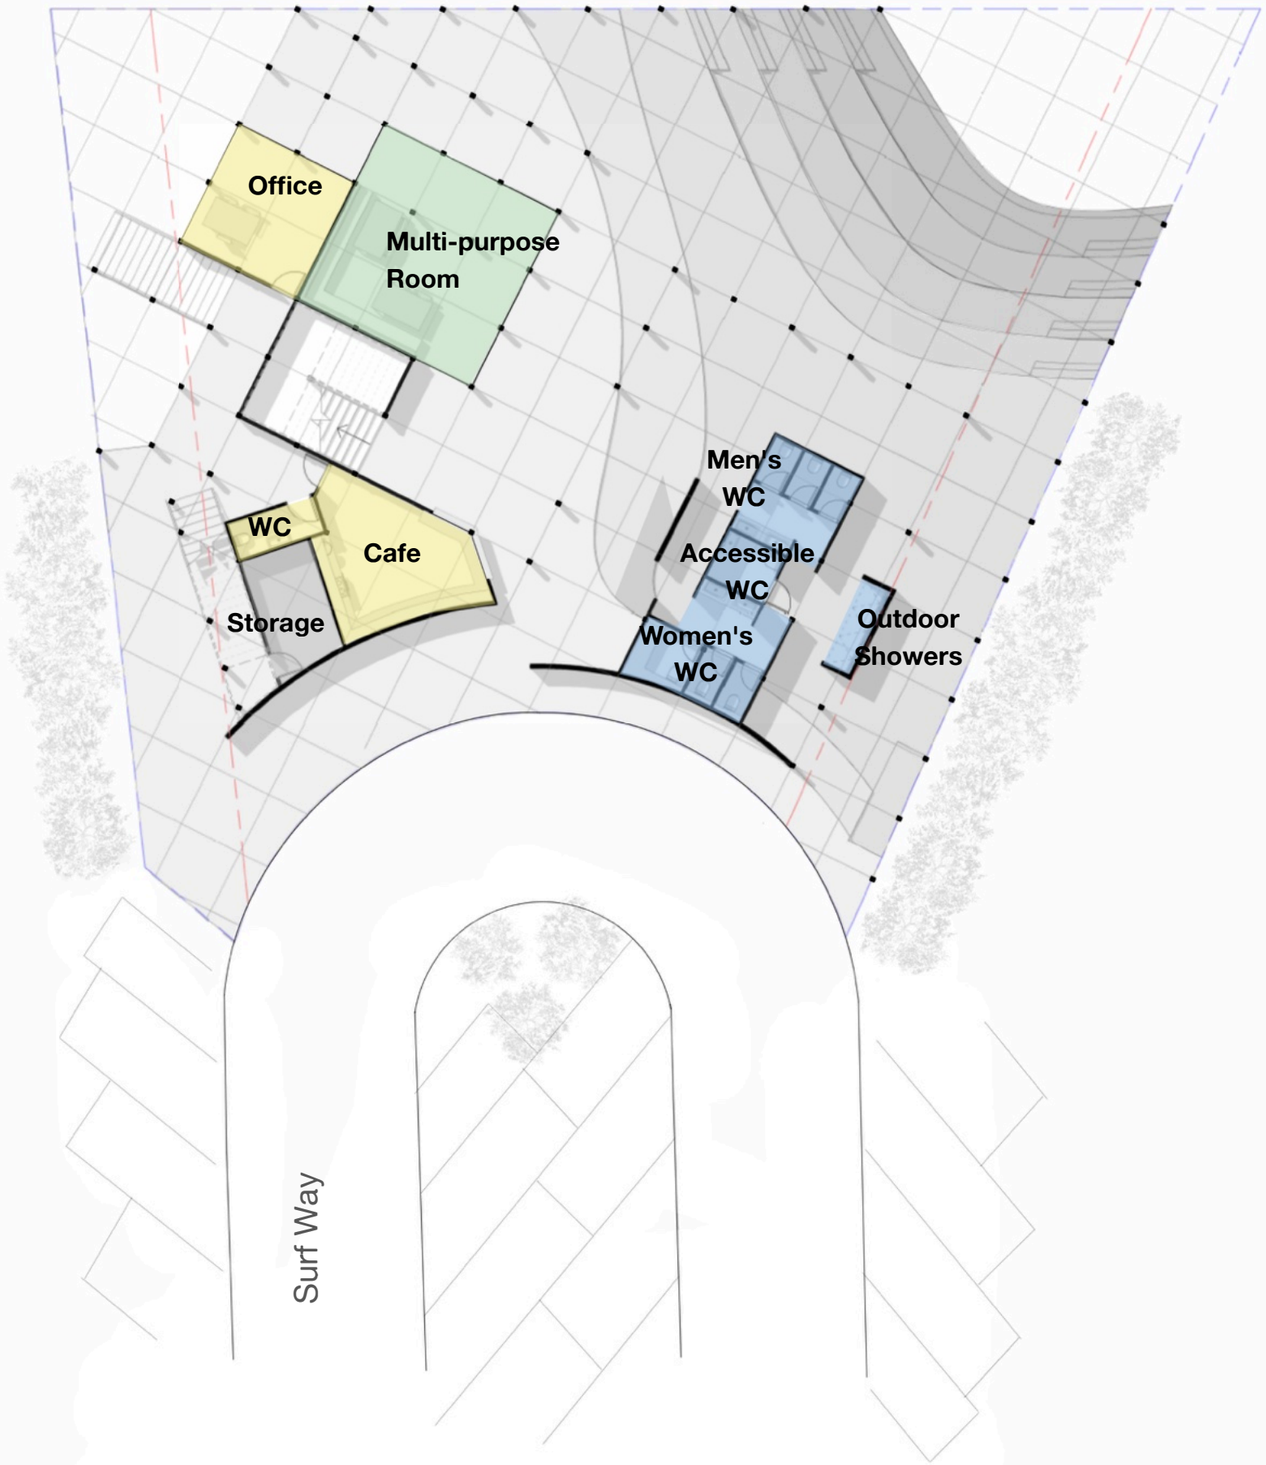

Public

Private


Semi-Public

Service

0 4 000 8 000mm

SCALE 1:200

Interior Views

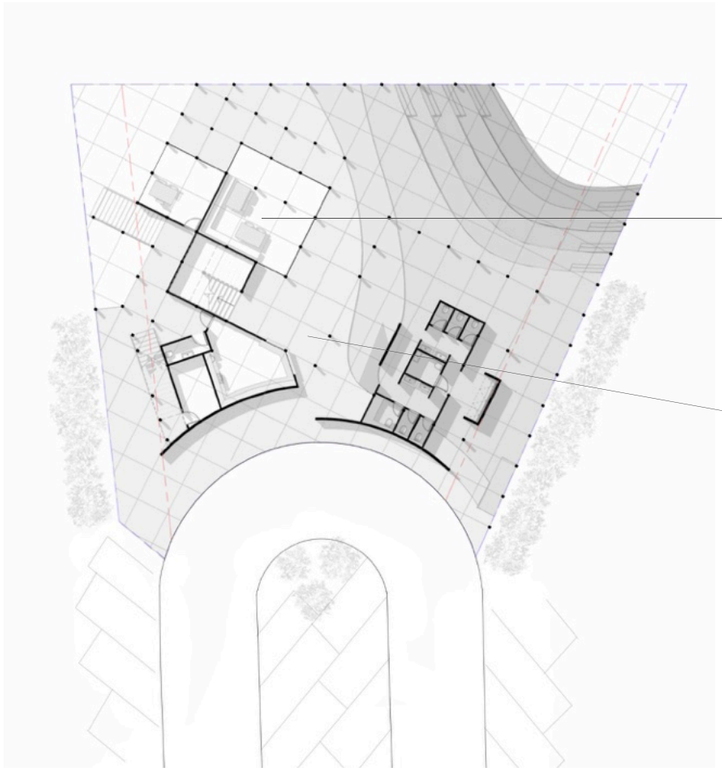



Multi-Purpose Room



Cafe

First Floor Plan

1:200

Long Beach




0 4 000 8 000mm

SCALE 1:200

First Floor Plan

Spatial Analysis 1:200

Long Beach

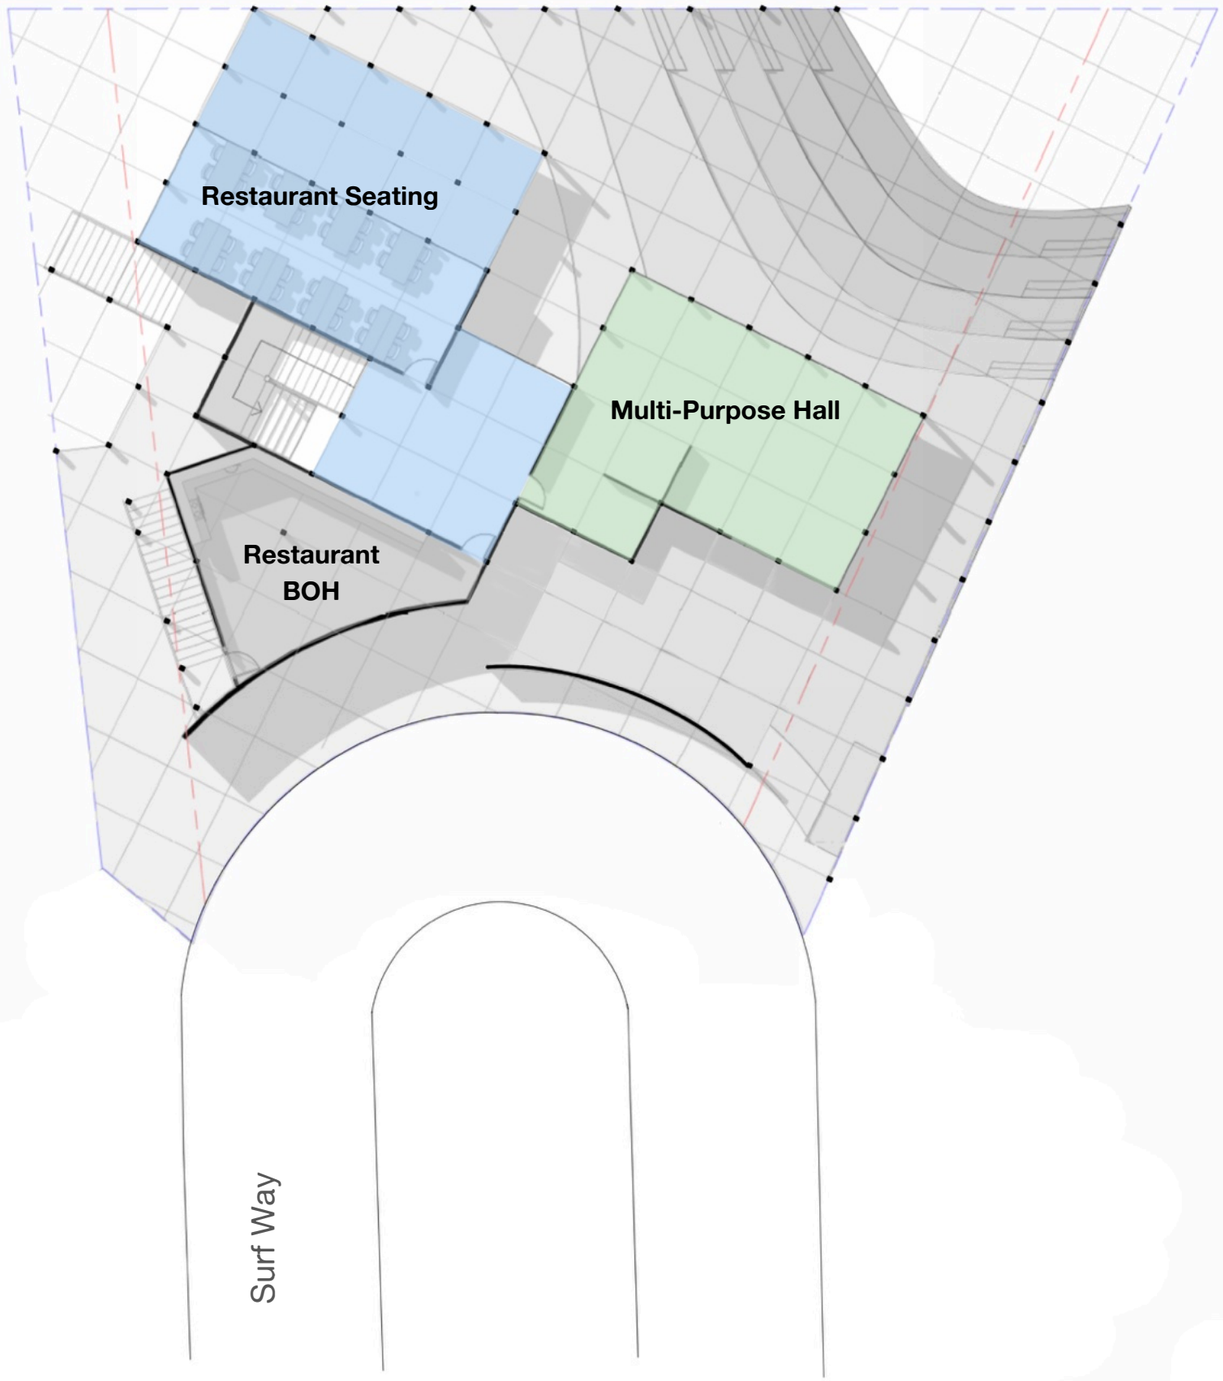

Public

Private


Semi-Public

Service

0 4 000 8 000mm

SCALE 1:200

Section A-A
1:100

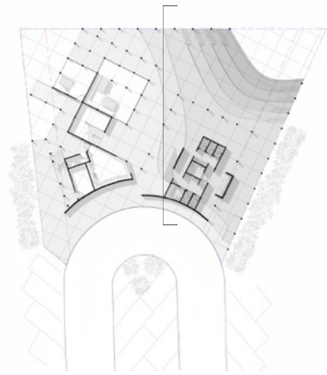




0 2 000 4 000mm
SCALE 1:100

Structural Axonometric

1:200

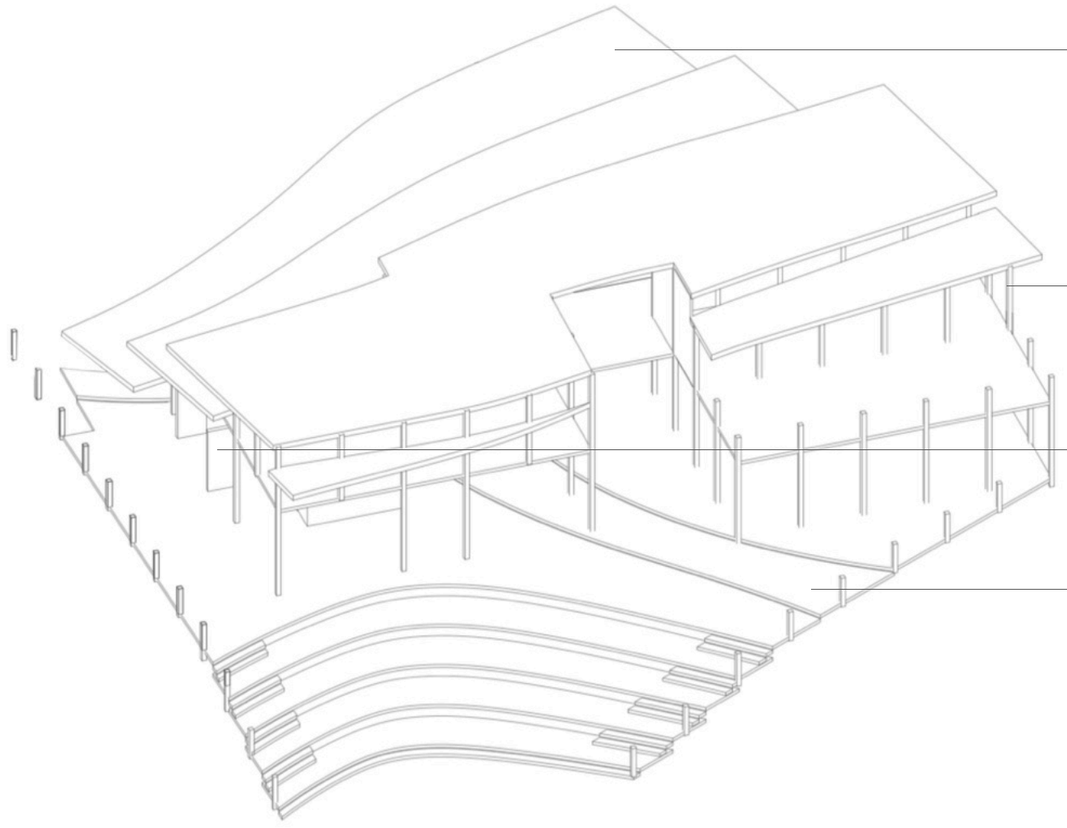

Roof

Metal

Beams + Columns

Beams: 75mm x 300mm

Columns: 150mm x 150mm

Walls

100mm CLT Eucalyptus Panels

65mm CLT Eucalyptus Panels,
used for light partitions

Floors

120mm CLT Eucalyptus Panels

0 4 000 8 000mm

SCALE 1:200

Exterior View


View from Surf Way Street



Exterior View

Birdseye view from NE



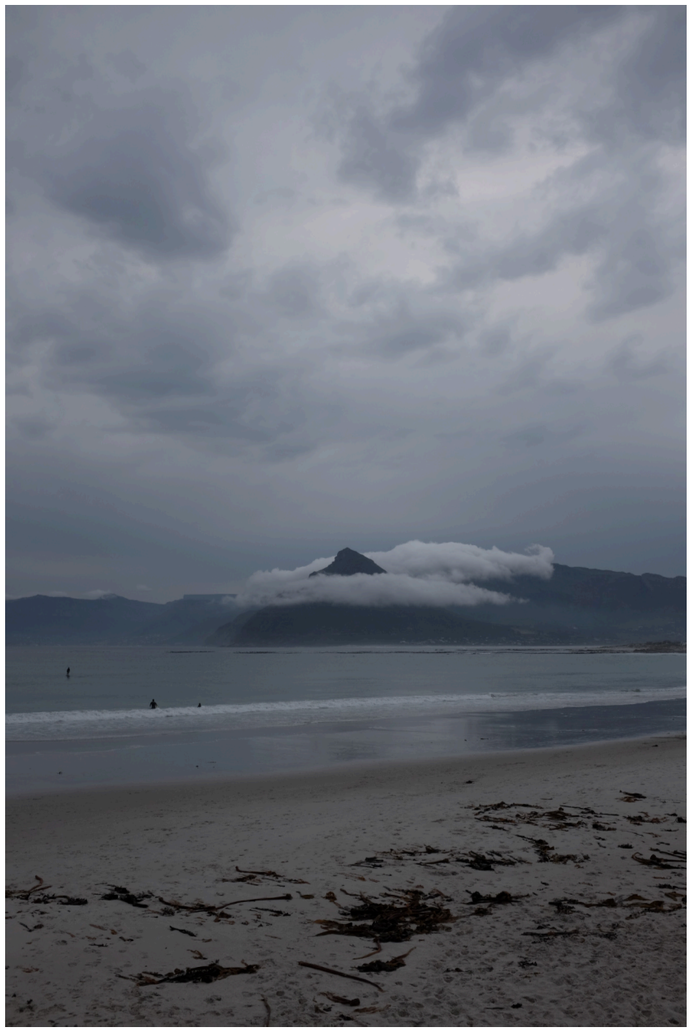


DO NOT
LITTER



